
PIANO 0

PIANO TERRA — INGRESSO, AULE, LABORATORI, PALESTRA E MENSA

Codici Locali 001 – 073 • Aule 014–022 • Lab. Linux (018), Multimediale (020-021), Lab 1-2, Officina (026)

I.T.T. «L. NEGRELLI» • I.T.G. «E. FORCELLINI»

POLO SCOLASTICO DI FELTRE (BL) — MAPPA DI ORIENTAMENTO

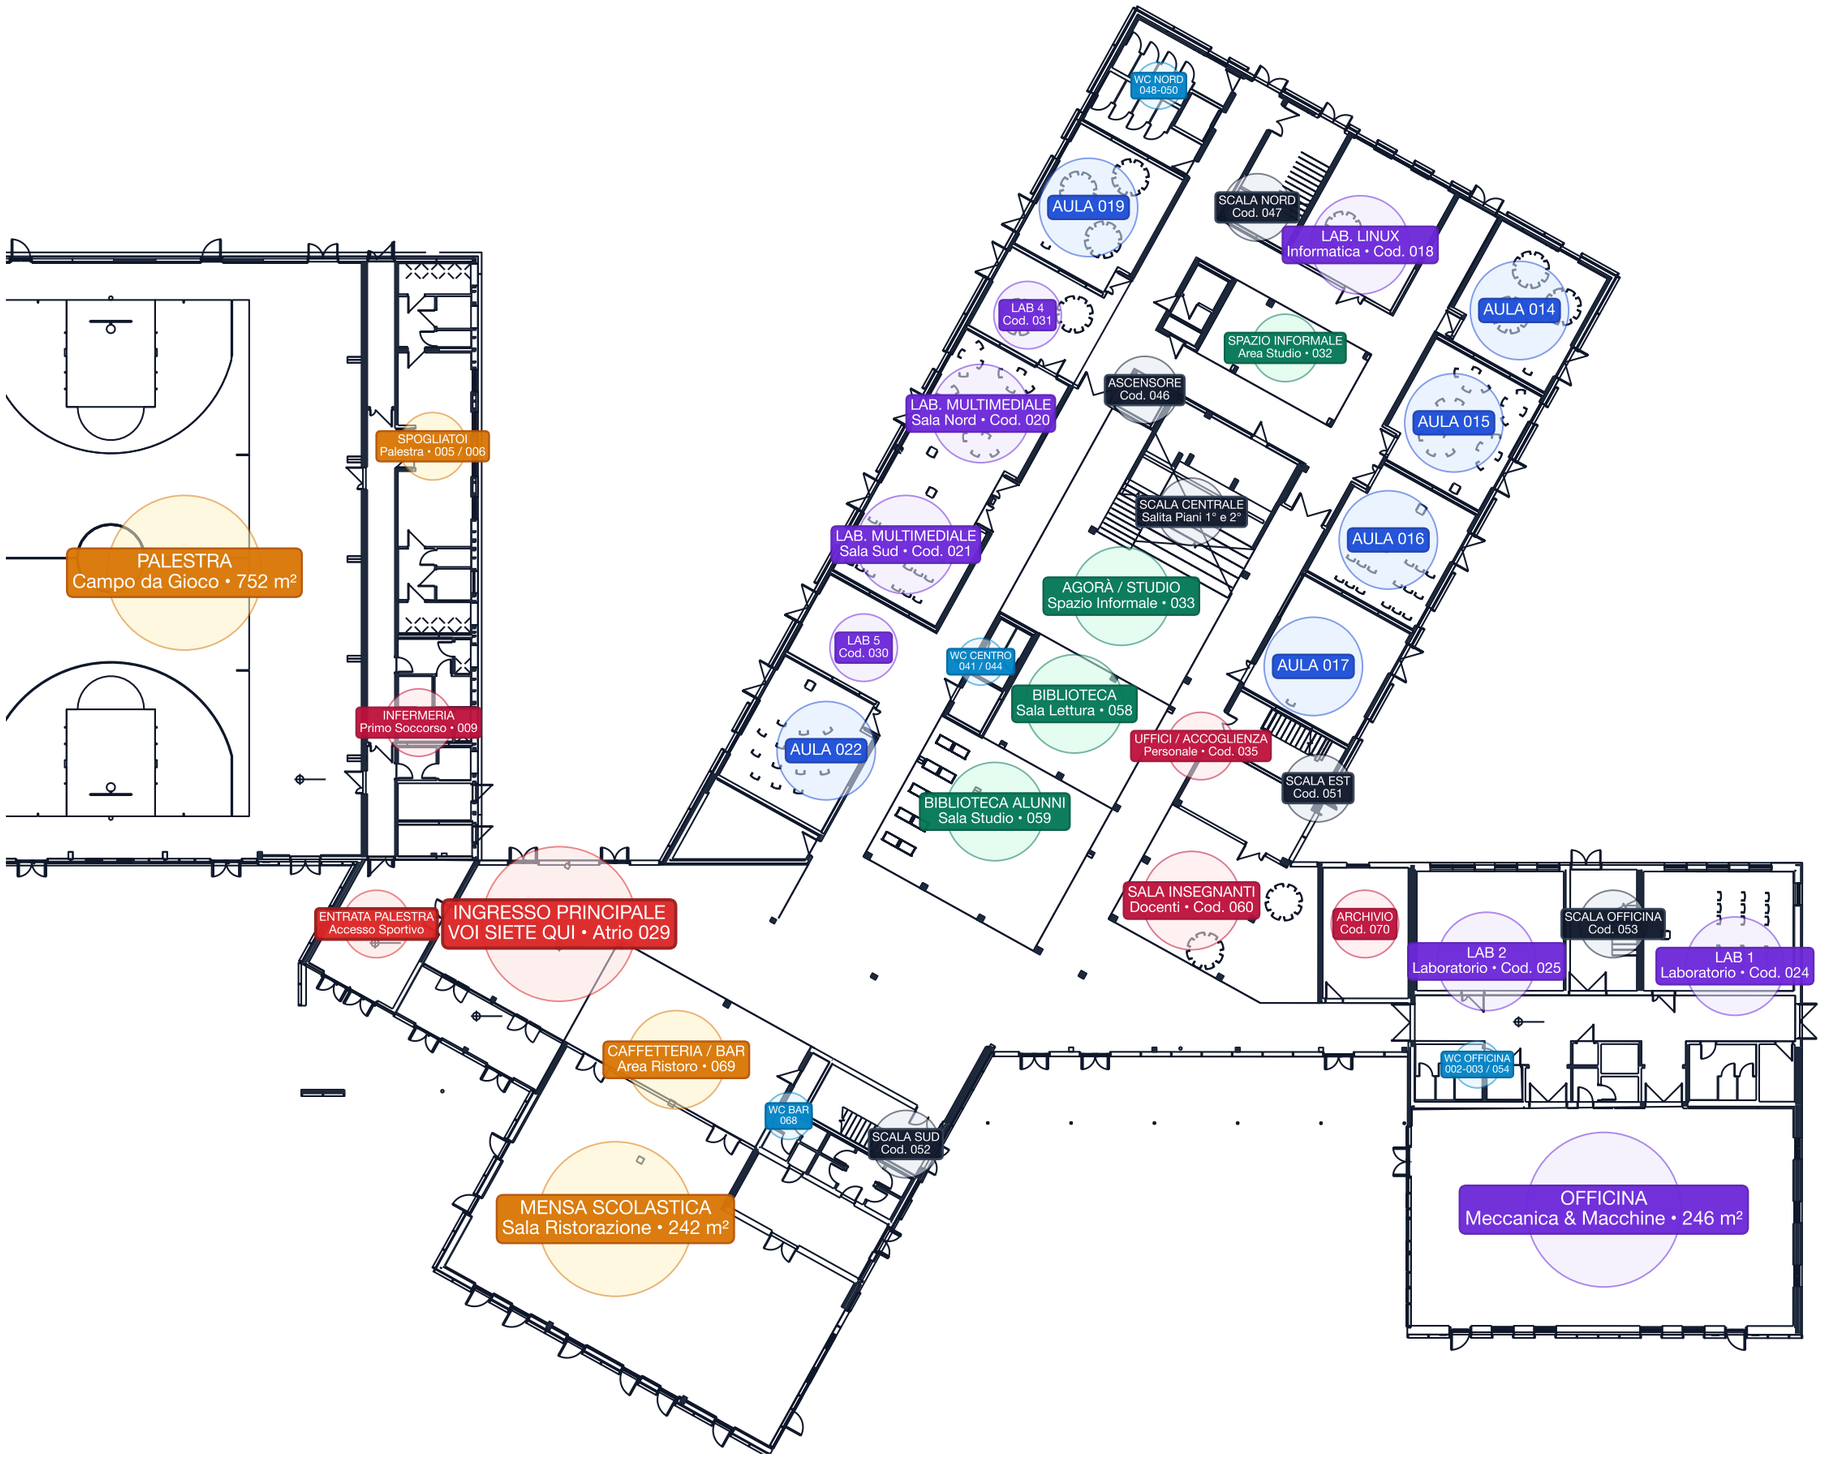

Ingressi / Voi Siete Qui

Aule Didattiche

Laboratori & Officina

Aule Informali & Biblioteca

Palestra, Mensa & Bar

Sala Docenti, Uffici & Infermeria

Scale & Ascensore

Servizi Igienici (WC)

ELENCO RAPIDO — PIANO TERRA

AULE DIDATTICHE (PIANO TERRA)

014	Aula 014
015	Aula 015
016	Aula 016
017	Aula 017
019	Aula 019
022	Aula 022

LABORATORI & OFFICINA

018	Lab. Linux (Ala Nord)
020-021	Lab. Multimediale (Ala Ovest)
024	Lab 1 (Blocco Est Officina)
025	Lab 2 (Blocco Est Officina)
026	Officina Meccanica (246 m²)
030 / 031	Lab 5 (030) e Lab 4 (031)

BIBLIOTECA & SPAZI STUDIO

058-059	Biblioteca Alunni (Centro)
032 / 033	Agorà & Spazi Informali

SPORT, RISTORO & SERVIZI

004	Palestra / Campo da Gioco
005-008	Spogliatoi Alunni e Docenti
028	Mensa Scolastica (Ala Sud)
069	Caffetteria / Bar (Atrio)

DOCENTI, UFFICI & SOCCORSO

060	Sala Insegnanti (Centro-Sud)
035	Uffici / Accoglienza
009	Infermeria (Lato Palestra)
070	Archivio (Lato Lab 2)

ACCESSI, SCALE & ASCENSORE

029 / 036	Ingresso Principale / Atrio
046	Ascensore Centrale (Piani 0-1-2)
047-053	Scale per Piano Primo e Secondo