
PIANO 1

I.T.T. «L. NEGRELLI» • I.T.G. «E. FORCELLINI» — POLO SCOLASTICO FELTRE

1° PIANO — AULE DIDATTICHE, LABORATORI, SEGRETERIA E VICEPRESIDENZA

ORIENTAMENTO & WAYFINDING
FORMATO STAMPA A3 B&W

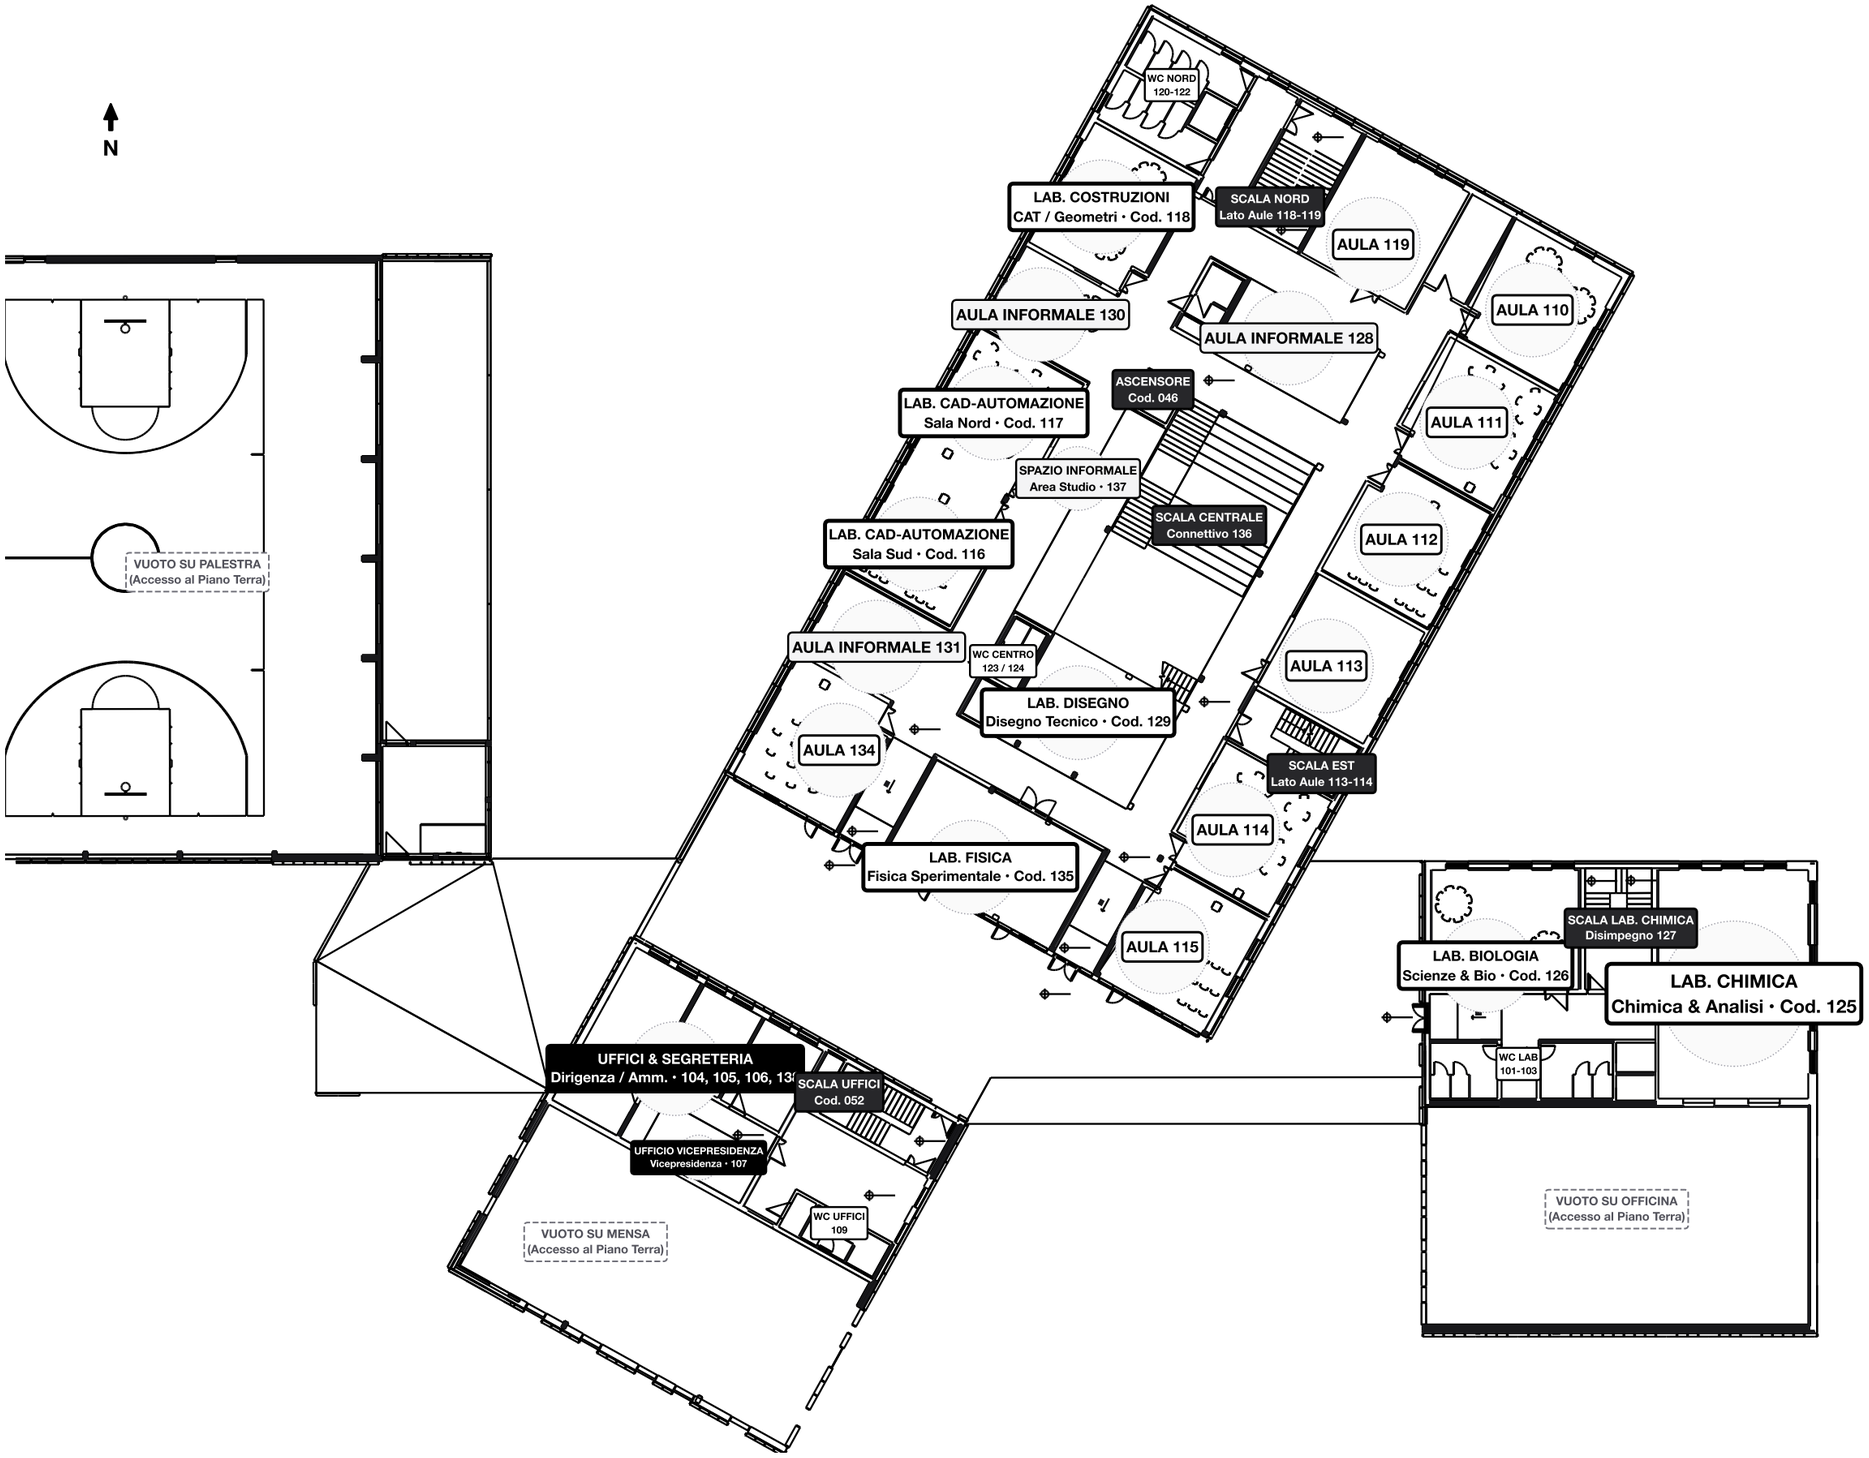

ELENCO LOCALI — PRIMO PIANO

AULE DIDATTICHE

110	Aula didattica (Ala Nord-Est)
111	Aula didattica (Ala Est)
112	Aula didattica (Ala Est)
113	Aula didattica (Ala Centro-Est)
114	Aula didattica (Ala Sud-Est)
115	Aula didattica (Ala Sud)
119	Aula didattica (Ala Nord)
134	Aula didattica (Ala Sud-Ovest)

GRANDI LABORATORI

116-117	Lab. CAD-Automaz. (Ovest)
118	Lab. Costruzioni (Nord-Ovest)
125	Lab. Chimica (Blocco Est)
126	Lab. Biologia (Blocco Est)
129	Lab. Disegno (Corpo Centro)
135	Lab. Fisica (Centro-Sud)

AULE INFORMALI & STUDIO

128	Aula Informale (Centro-Nord)
130	Aula Informale (Ala Ovest)
131	Aula Informale (Ala Ovest)
137	Spazio Studio Connettivo

DIRIGENZA, UFFICI & ACCESSI

104-106	**Uffici & Segreteria (Sud-Ovest)**
107	**Ufficio Vicepresidenza (Sud-Ovest)**
046	Ascensore Centrale (Tutti i piani)
SCALE	Scale Principali (Nord, Centro, Est)

[AULA]	Aule Didattiche (Bordo nero sottile)	**[LAB]**	Laboratori / Officina (Bordo nero spesso)	**[INGRESSO]**	Ingressi (Fondo nero, testo bianco)
[UFFICI]	Uffici & Vicepresidenza (Fondo nero)	**[INFORMALE]**	Spazi Studio (Fondo grigio chiaro)	**[WC]**	Servizi Igienici (Cod. WC)