
PIANO 2

I.T.T. «L. NEGRELLI» • I.T.G. «E. FORCELLINI» — POLO SCOLASTICO FELTRE

2° PIANO — AULE DIDATTICHE, INFORMATICA, ELETTRONICA, SISTEMI E LINGUE

ORIENTAMENTO & WAYFINDING
FORMATO STAMPA A3 B&W

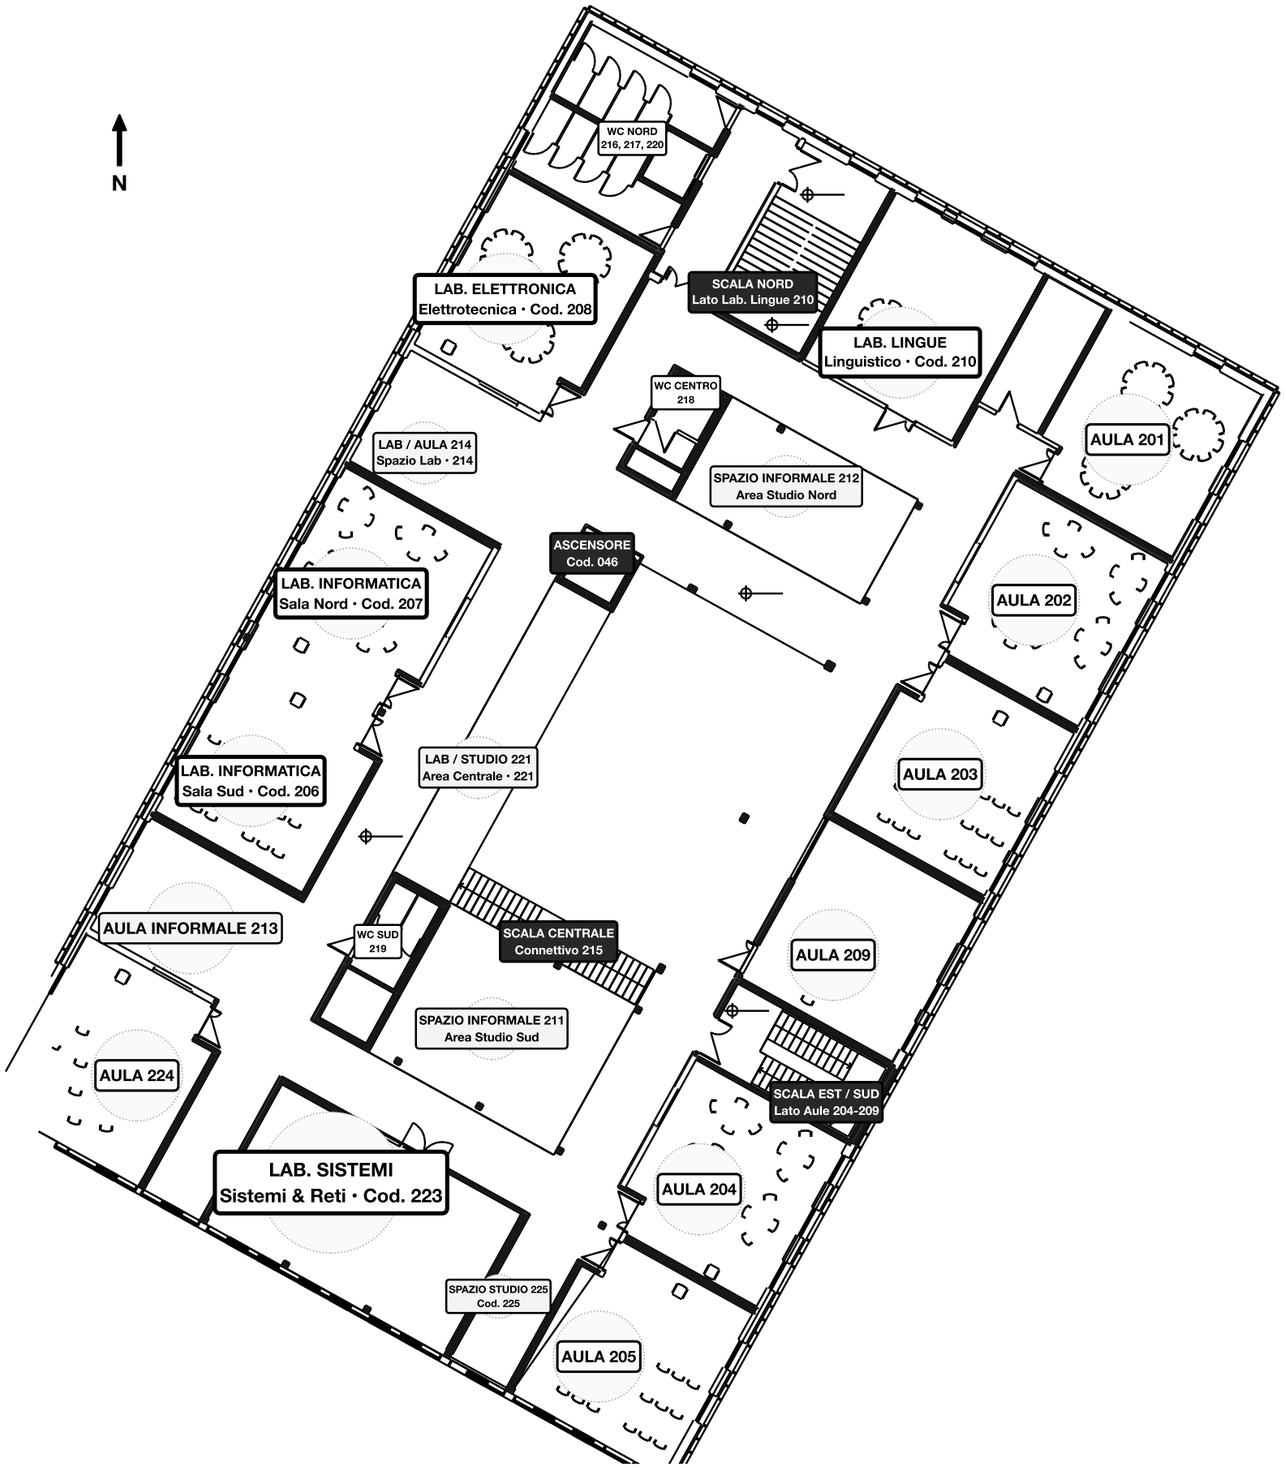

ELENCO LOCALI — SECONDO PIANO

AULE DIDATTICHE

201	Aula didattica (Ala Nord-Est)
202	Aula didattica (Ala Est)
203	Aula didattica (Ala Est)
204	Aula didattica (Ala Sud-Est)
205	Aula didattica (Ala Sud)
209	Aula didattica (Ala Centro-Est)
224	Aula didattica (Ala Sud-Ovest)

LABORATORI SPECIALISTICI

206	Lab. Informatica Sud (Ala Ovest)
207	Lab. Informatica Nord (Ala Ovest)
208	Lab. Elettronica (Nord-Ovest)
210	Lab. Lingue (Ala Nord)
223	Lab. Sistemi & Reti (Ala Sud)

AULE INFORMALI & STUDIO

213	Aula Informale (Ala Ovest)
214	Laboratorio / Aula (Ala Ovest)
221	Laboratorio / Studio (Centro)
211-212	Spazi Studio (Nord & Sud)
225	Spazio Studio (Ala Sud)

CONNETTIVO & SERVIZI

046	Ascensore Centrale (Tutti i piani)
215	Scala Centrale / Connettivo
SCALE	Scale Nord e Sud di Sicurezza
WC	Servizi Igienici (Nord, Centro, Sud)

[AULA]	Aule Didattiche (Bordo nero sottile)	**[LAB]**	Laboratori / Officina (Bordo nero spesso)	**[INGRESSO]**	Ingressi (Fondo nero, testo bianco)
[UFFICI]	Uffici & Vicepresidenza (Fondo nero)	**[INFORMALE]**	Spazi Studio (Fondo grigio chiaro)	**[WC]**	Servizi Igienici (Cod. WC)